

PROJETO FOTOVOLTAICO 5,04 kWp

Nota: Este documento contém dados pessoais (RG e CPF) ou (CNPJ). A Plataforma *Idealtech* protege seus dados, seguindo as normativas de proteção de dados conforme a Lei nº 13.709/2018 (LGPD). Contudo, após o *download*, a responsabilidade passa a ser do cliente/empresa.


Cliente: CAINAN DIEGO DE ANDRADE
Unidade consumidora: 55154392
Data: 1 de abril de 2025
Revisão: 1
Execução: Diego Lima
Revisão: Guildo Sena
Aprovação: Guildo Sena CFT 033215

DOCUMENTO DE INSTALAÇÃO

Olá, sou o Teslinha, estou aqui para informar que seu projeto está na nossa plataforma salva com a maior segurança para sua empresa e seu cliente. A Ideal Tech Brasil é uma empresa que traz segurança conforme a LGPD – Lei Geral de Proteção de Dados. Nosso banco de dados e antivírus são licenciados pela *Microsoft*, onde garante maior segurança no mercado da TI. Nossa engenharia apresenta o melhor *know-how* na área de Engenharia Elétrica. Nossa empresa apresenta cadastro nos conselhos CFT e CREA.



Linha do projeto:

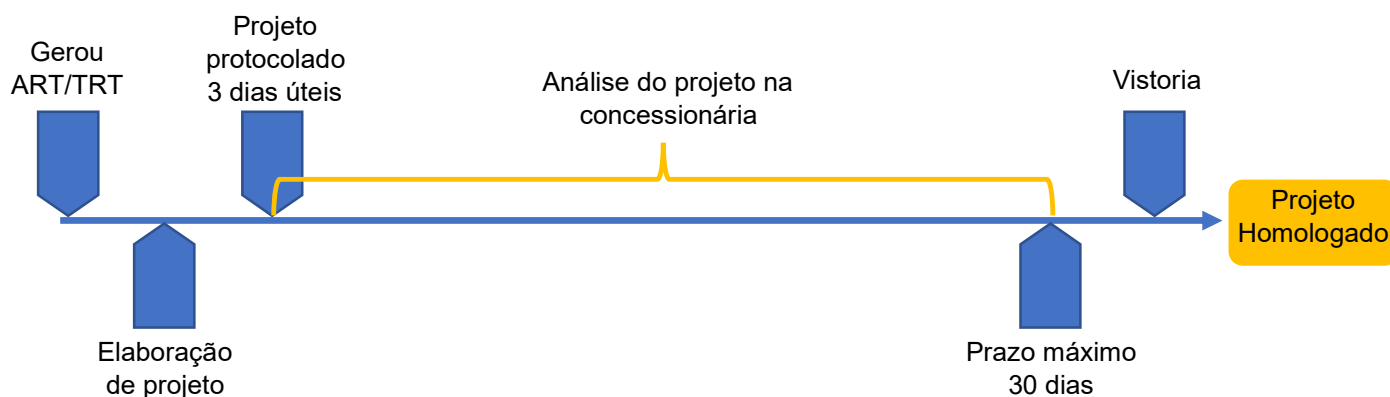


Normativas:

ABNT 5410
ABNT 16690


Anexos:

TRT-CFT
Desenho Unifilar
Protocolo da concessionária

DETALHES DA INSTALAÇÃO

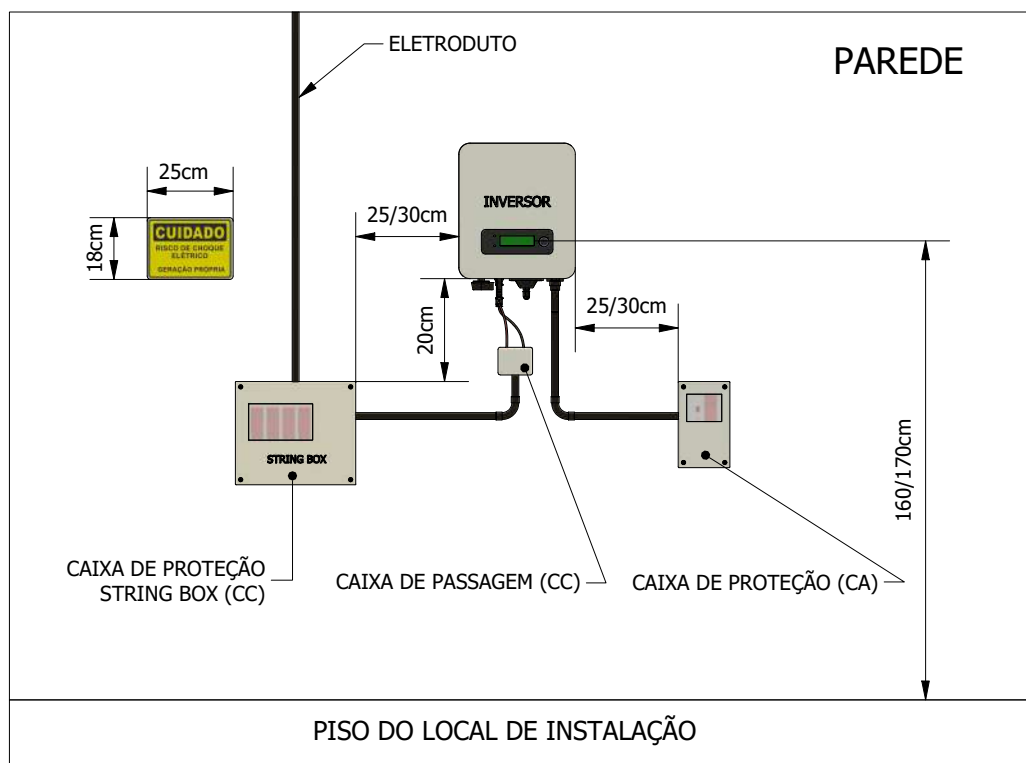

VISTA GERAL

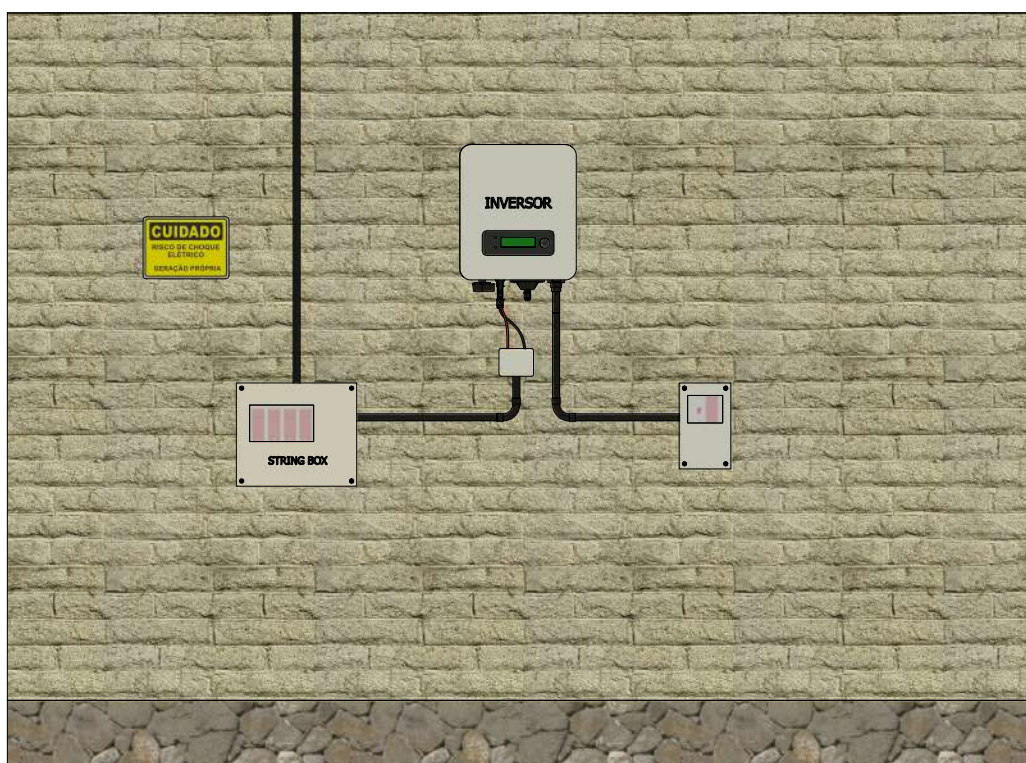

NOTA DE ENGENHARIA:

1. AS DISTÂNCIAS ENTRE O INVERSOR, STRING BOX CC E CAIXA DE PROTEÇÃO CA SÃO MEDIDAS DE SEGURANÇA, CASO OCORRA UM CURTO-CIRCUITO.
2. COLOCAR PLACA DE ADVERTÊNCIA PRÓXIMO À INSTALAÇÃO DO SISTEMA.
3. EVITAR INSTALAR O SISTEMA PRÓXIMO À LINHAS DE GÁS OU BOTTIÕES DE GÁS.
4. INSTALAR O SISTEMA EM LOCAL VENTILADO.



A LEI nº 9.610/1998, DIREITOS AUTORAIS, ASSIM COLOCANDO O USO EXCLUSIVO PARA O DEPARTAMENTO TÉCNICO DA EMPRESA E DA CONCESSIONÁRIA DESTE DOCUMENTO. AUTORIA DE RESPONSABILIDADE DA IDEAL TECH BRASIL.
Este documento não pode ser copiado (Xerox ou fotocópia por aparelhos eletrônicos) sem a permissão por escrito muito menos cedido para terceiros para propósitos não autorizados. Punições previstas em lei.

PROJETO:

INSTALAÇÃO PARA INVERSORES

EXECUÇÃO: TÁSSIO ANDRADE NEVES

REVISÃO: GUILDO SENA

APROVAÇÃO: GUILDO SENA

CREA: 60019BA

IMPRESSÃO:

A4

PAGINA:

1

DATA: 04/10/2022

REVISÃO: 0



Termo de Responsabilidade Técnica - TRT
Lei nº 13.639, de 26 de MARÇO de 2018

CRT 04

TRT OBRA / SERVIÇO
Nº CFT2504371774

Conselho Regional dos Técnicos Industriais 04

INICIAL

1. Responsável Técnico(a)

GUILDO DOS SANTOS DE SENA

Título profissional: **TÉCNICO EM MECATRÔNICA, TÉCNICO EM SISTEMAS DE ENERGIA RENOVÁVEL**

Registro: **03321561506**

2. Contratante

Contratante: **EKOH ENERGIAS**

CPF/CNPJ: **35.259.576/0001-52**

Logradouro: **RUA 21**

Nº: **17**

Complemento:

Bairro: **AREIAS**

Cidade: **TIJUCAS**

UF: **SC**

CEP: **88200000**

País: **Brasil**

Telefone:

Email:

Contrato: **Não especificado**

Celebrado em:

Valor: **R\$ 680,00**

Tipo de contratante: **PESSOA JURIDICA DE DIREITO PRIVADO**

Ação Institucional: **NENHUM**

3. Dados da Obra/Serviço

Logradouro: **RUA 06**

Nº: **403**

Complemento: **casa 03 - LOT BR. FELICE, B**

Bairro: **AREIAS**

Cidade: **TIJUCAS**

UF: **SC**

CEP: **88200000**

Telefone:

Email:

Coordenadas Geográficas: **Latitude: 27°13'52.45"S Longitude: 48°38'24.26"W**

Data de Início: **11/03/2025**

Previsão de término: **09/06/2025**

Finalidade: **Residencial**

Proprietário(a): **CAINAN DIEGO DE ANDRADE**

CPF/CNPJ: **078.252.929-10**

4. Atividade Técnica

13 - PROJETO

Quantidade

Unidade

96 - ELABORAÇÃO > CFT -> OBRAS E SERVIÇOS - ELÉTRICA -> ELETROTÉCNICA APLICADA
 -> GERAÇÃO DE ENERGIA -> #1789 - SOLAR FOTOVOLTAICA

5,040

kWp

2 - EXECUÇÃO

Quantidade

Unidade

15 - EXECUÇÃO > CFT -> OBRAS E SERVIÇOS - ELÉTRICA -> ELETROTÉCNICA APLICADA ->
 GERAÇÃO DE ENERGIA -> #1789 - SOLAR FOTOVOLTAICA

5,040

kWp

Após a conclusão das atividades técnicas o(a) profissional deverá proceder a baixa deste TRT

5. Observações

SISTEMA FOTOVOLTAICO LIGADO A CONCESSIONARIA CELESC;/INATIVO CAINAN DIEGO DE ANDRADE - TIJUCAS - SC - 3828 - EKOH ENERGIAS

6. Informações Adicionais

Valor do TRT: **R\$ 64,89**

Pago em: **11/03/2025**

Boleto: **8248362307**

Registrada em: **11/03/2025**


7. Assinaturas

Declaro serem verdadeiras as informações acima


Responsável Técnico: **GUILDO DOS SANTOS DE SENA**
 CPF: **033.215.615-06**

Contratante: **EKOH ENERGIAS**
 CNPJ: **35.259.576/0001-52**



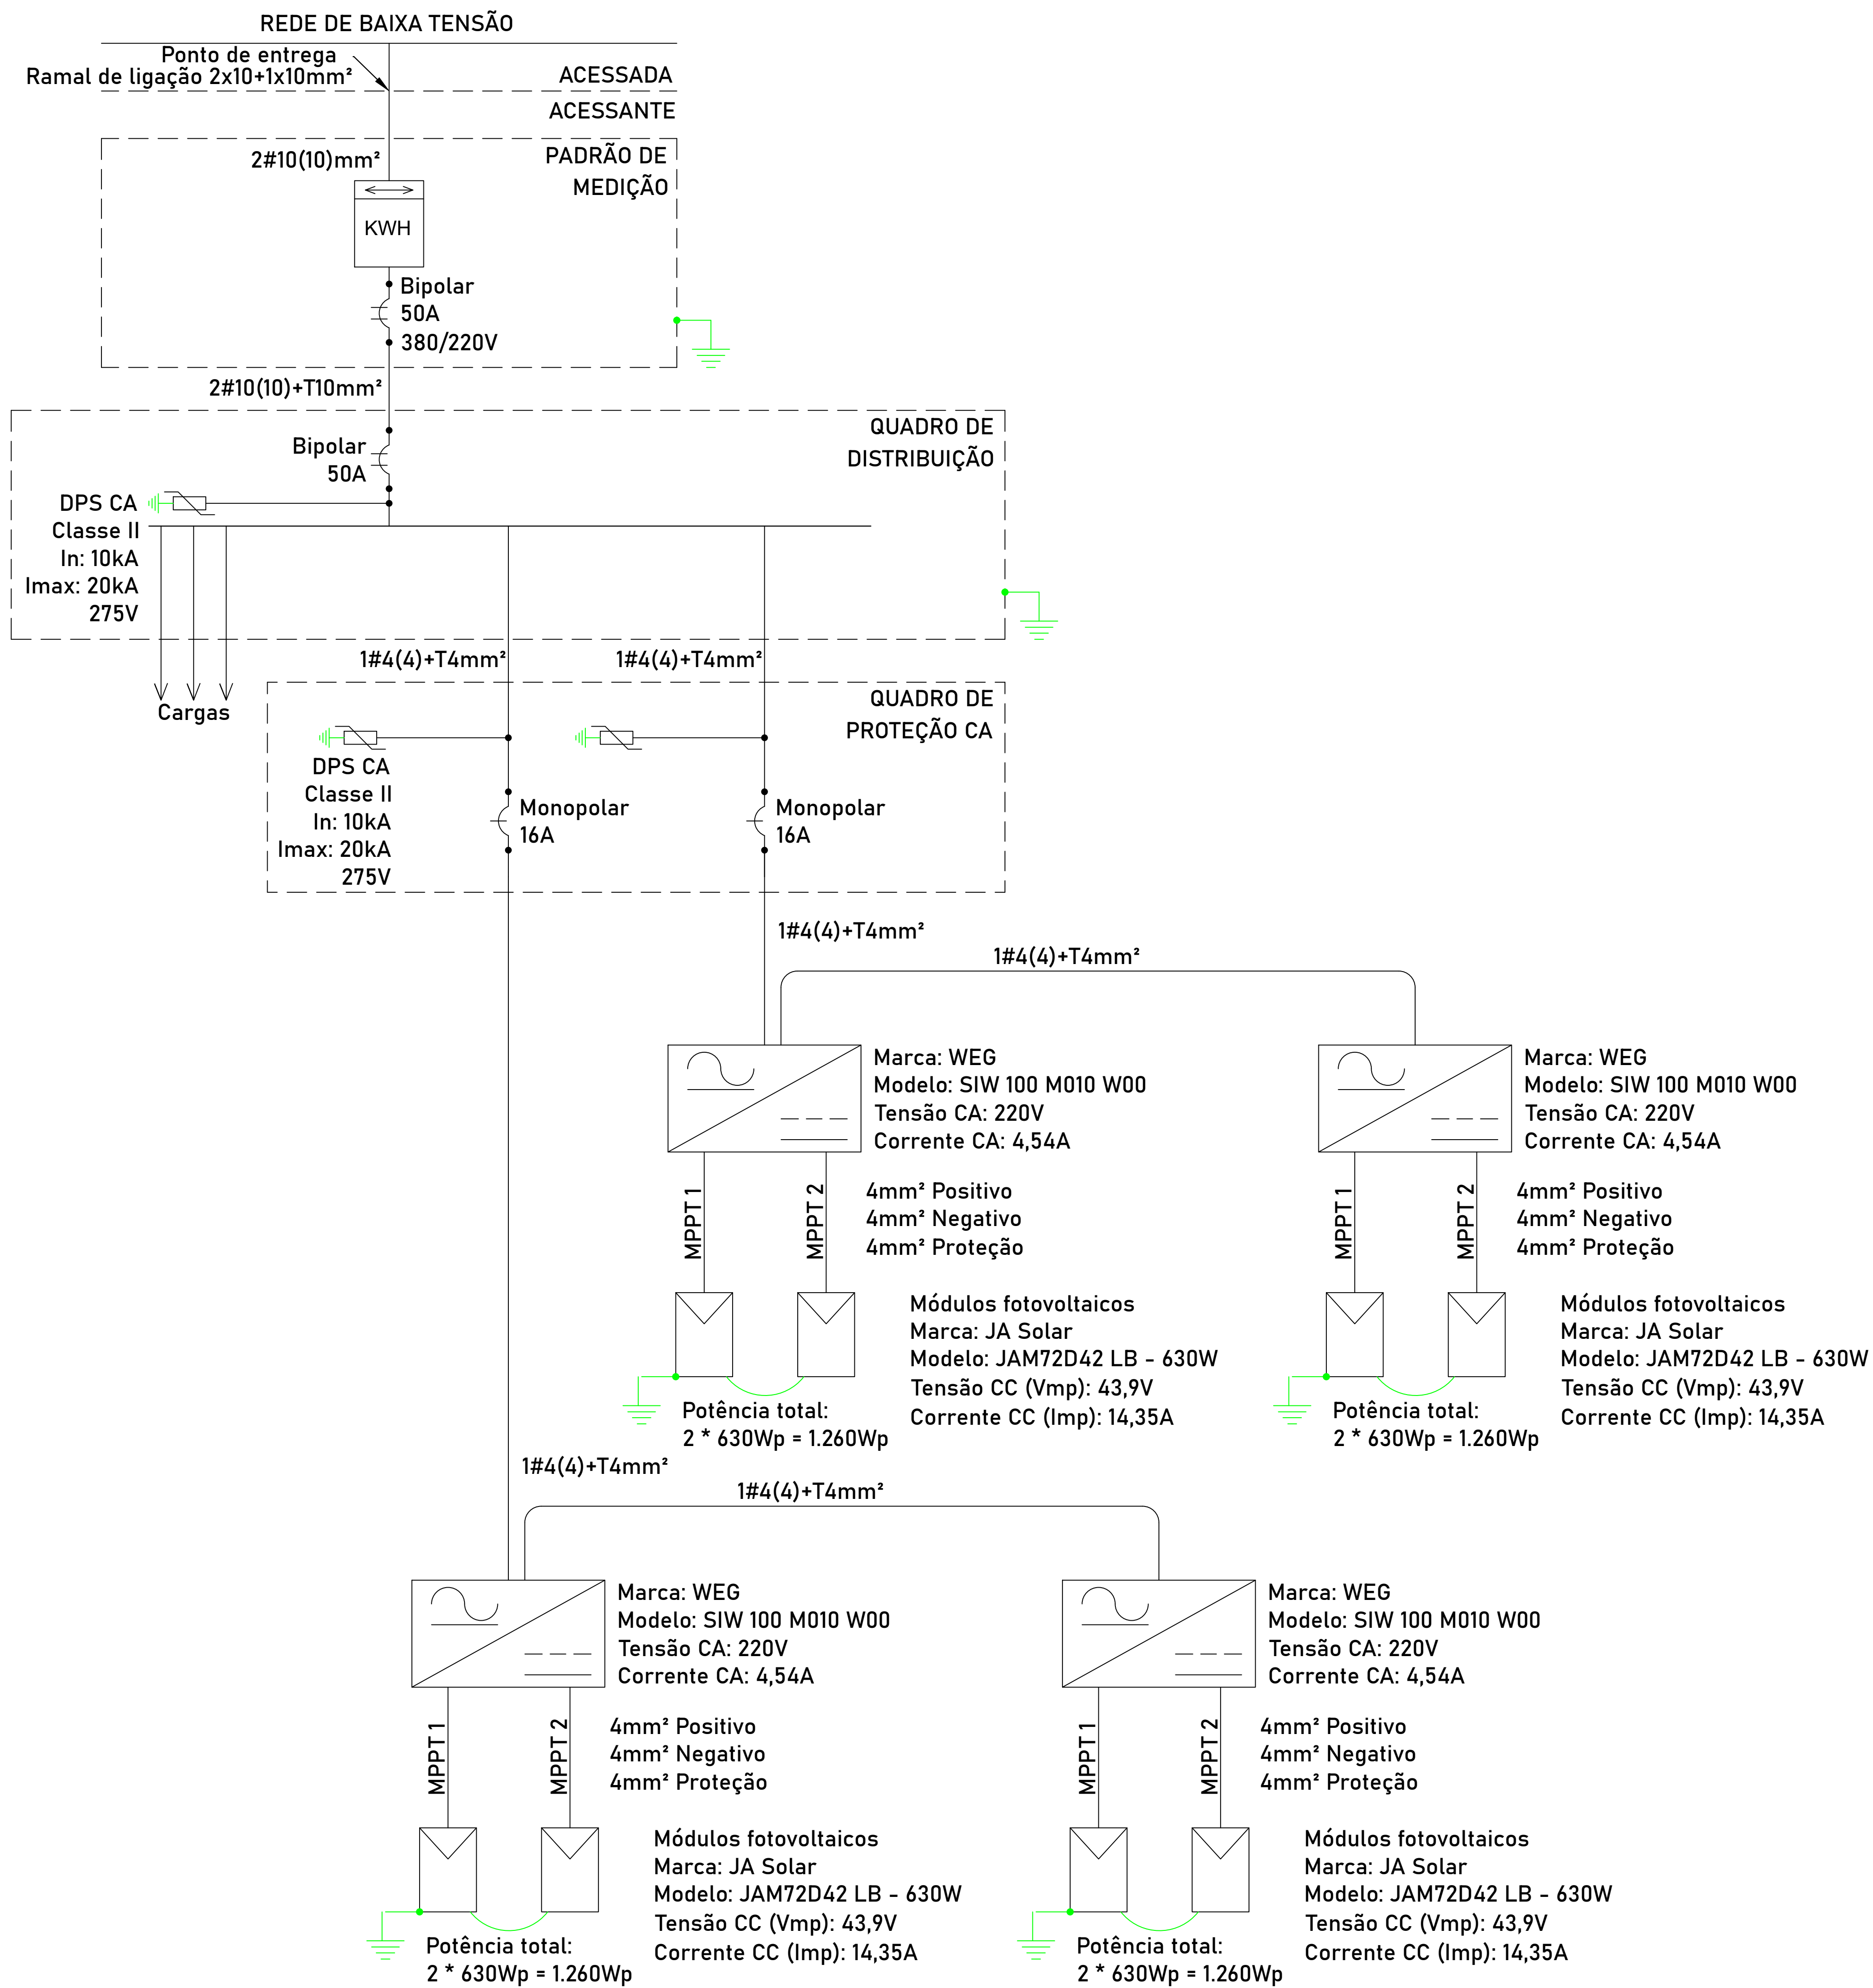

LEGENDA	
	Disjuntor termomagnético
	Medidor de energia kWh
	DPS CC / CA
	Fusível CC
	Barramento
	Transformador / Autotransformador
	Inversor / Microinversor
	Módulo fotovoltaico

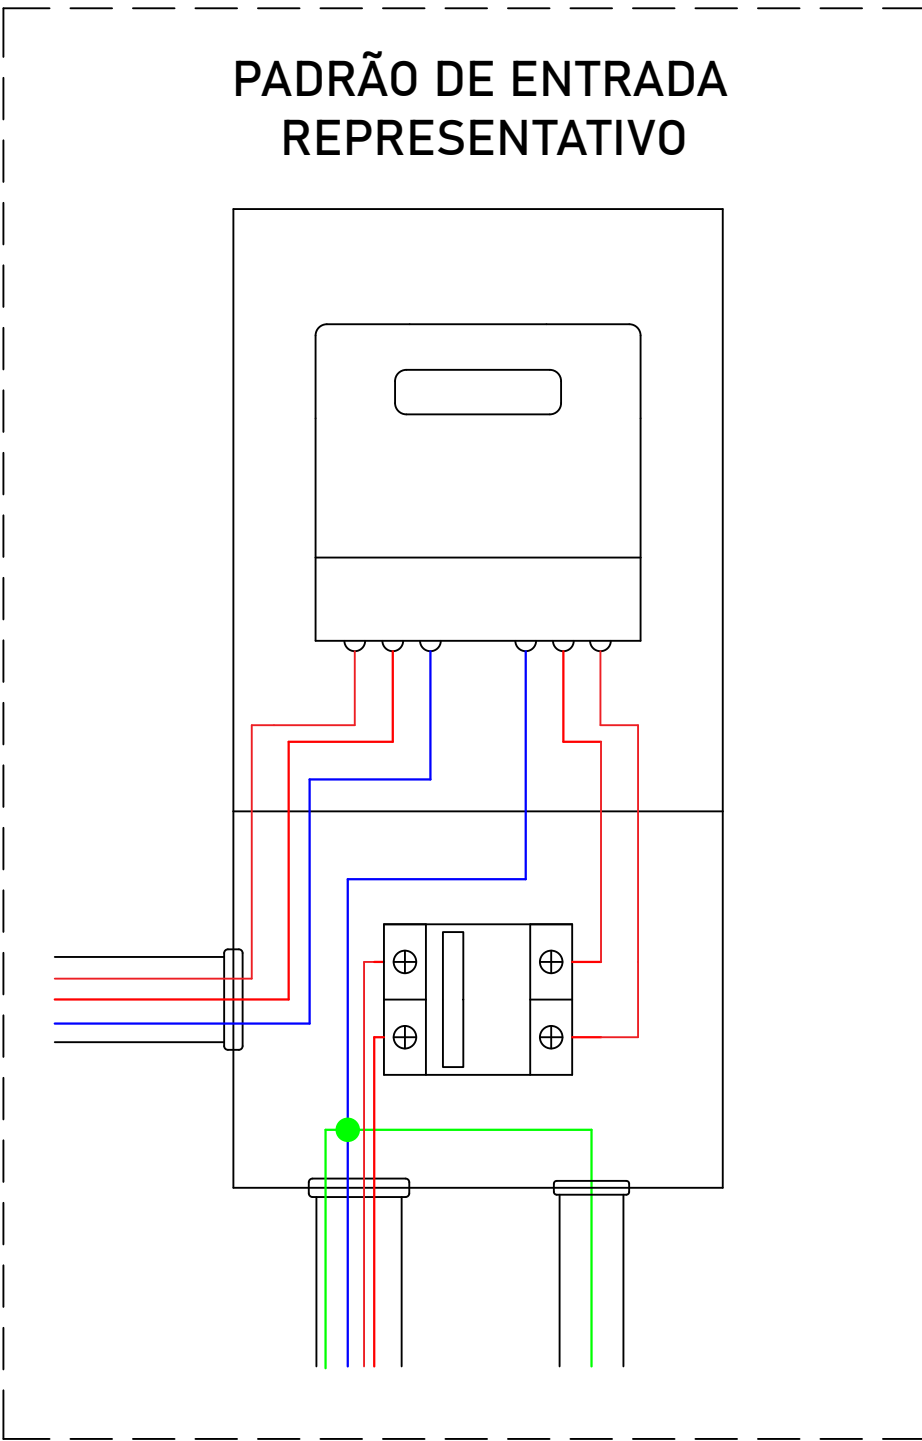


- NOTAS:
1. A seção transversal dos condutores foram dimensionadas em função da corrente máxima de saída e capacidade de condução de corrente, permitindo-se utilizar até uma faixa acima da descrita em cada trecho dessa planta (exceto no padrão de medição);
 2. Cabos em corrente contínua, na tensão elétrica máxima de 1,8kV, isolamento em XLPE e cobertura em XLPE (termofixo) com UV;
 3. Cabos em corrente alternada, na tensão máxima de 1kV, isolamento e cobertura em PCV;
 4. Cada string será protegida individualmente, através das proteções internas do inversor ou por fusível e DPS CC;
 5. A seção transversal dos condutores foram dimensionadas em função da corrente máxima de saída e capacidade de condução de corrente, permitindo-se utilizar até uma faixa acima da descrita em cada trecho dessa planta (exceto no padrão de medição);
 6. Cada MPPT possui apenas uma entrada.


MICROINVERSORES DE 01 A 04

MPPT 01 • STRING 01 Quant. de módulos: 01 unidade Tensão (Vmp): 43,9 * 1 = 43,9V Corrente (Imp): 14,35A Potência total: 630Wp * 1 = 630Wp	MPPT 02 • STRING 01 Quant. de módulos: 01 unidade Tensão (Vmp): 43,9 * 1 = 43,9V Corrente (Imp): 14,35A Potência total: 630Wp * 1 = 630Wp
--	--

 PLATAFORMA DE PROJETOS E ENGENHARIA		 Assinatura do responsável técnico Guíldio dos Santos de Sena CFT BA 03321561506	
PROJETO:	Sistema fotovoltaico 5,04kWp	PROPRIETÁRIO: Nome do cliente: Cainan Diego de Andrade CNPJ/CPF: 078.252.929-10	ID do pedido: 3828
TÍTULO:	DIAGRAMA UNIFILAR	ENDEREÇO DA OBRA: Endereço: RUA 06, 403- LOT BR. FELICE, B - AREIAS - TIJUCAS CEP: 88.200-000	
PROJETISTA: Diego Lima	DATA: 17/03/2025	REVISADO POR: Guíldio Sena	REVISÃO: 01
CONTA CONTRATO:	55154392	INTEGRADOR: Ekoh	FOLHA: 01

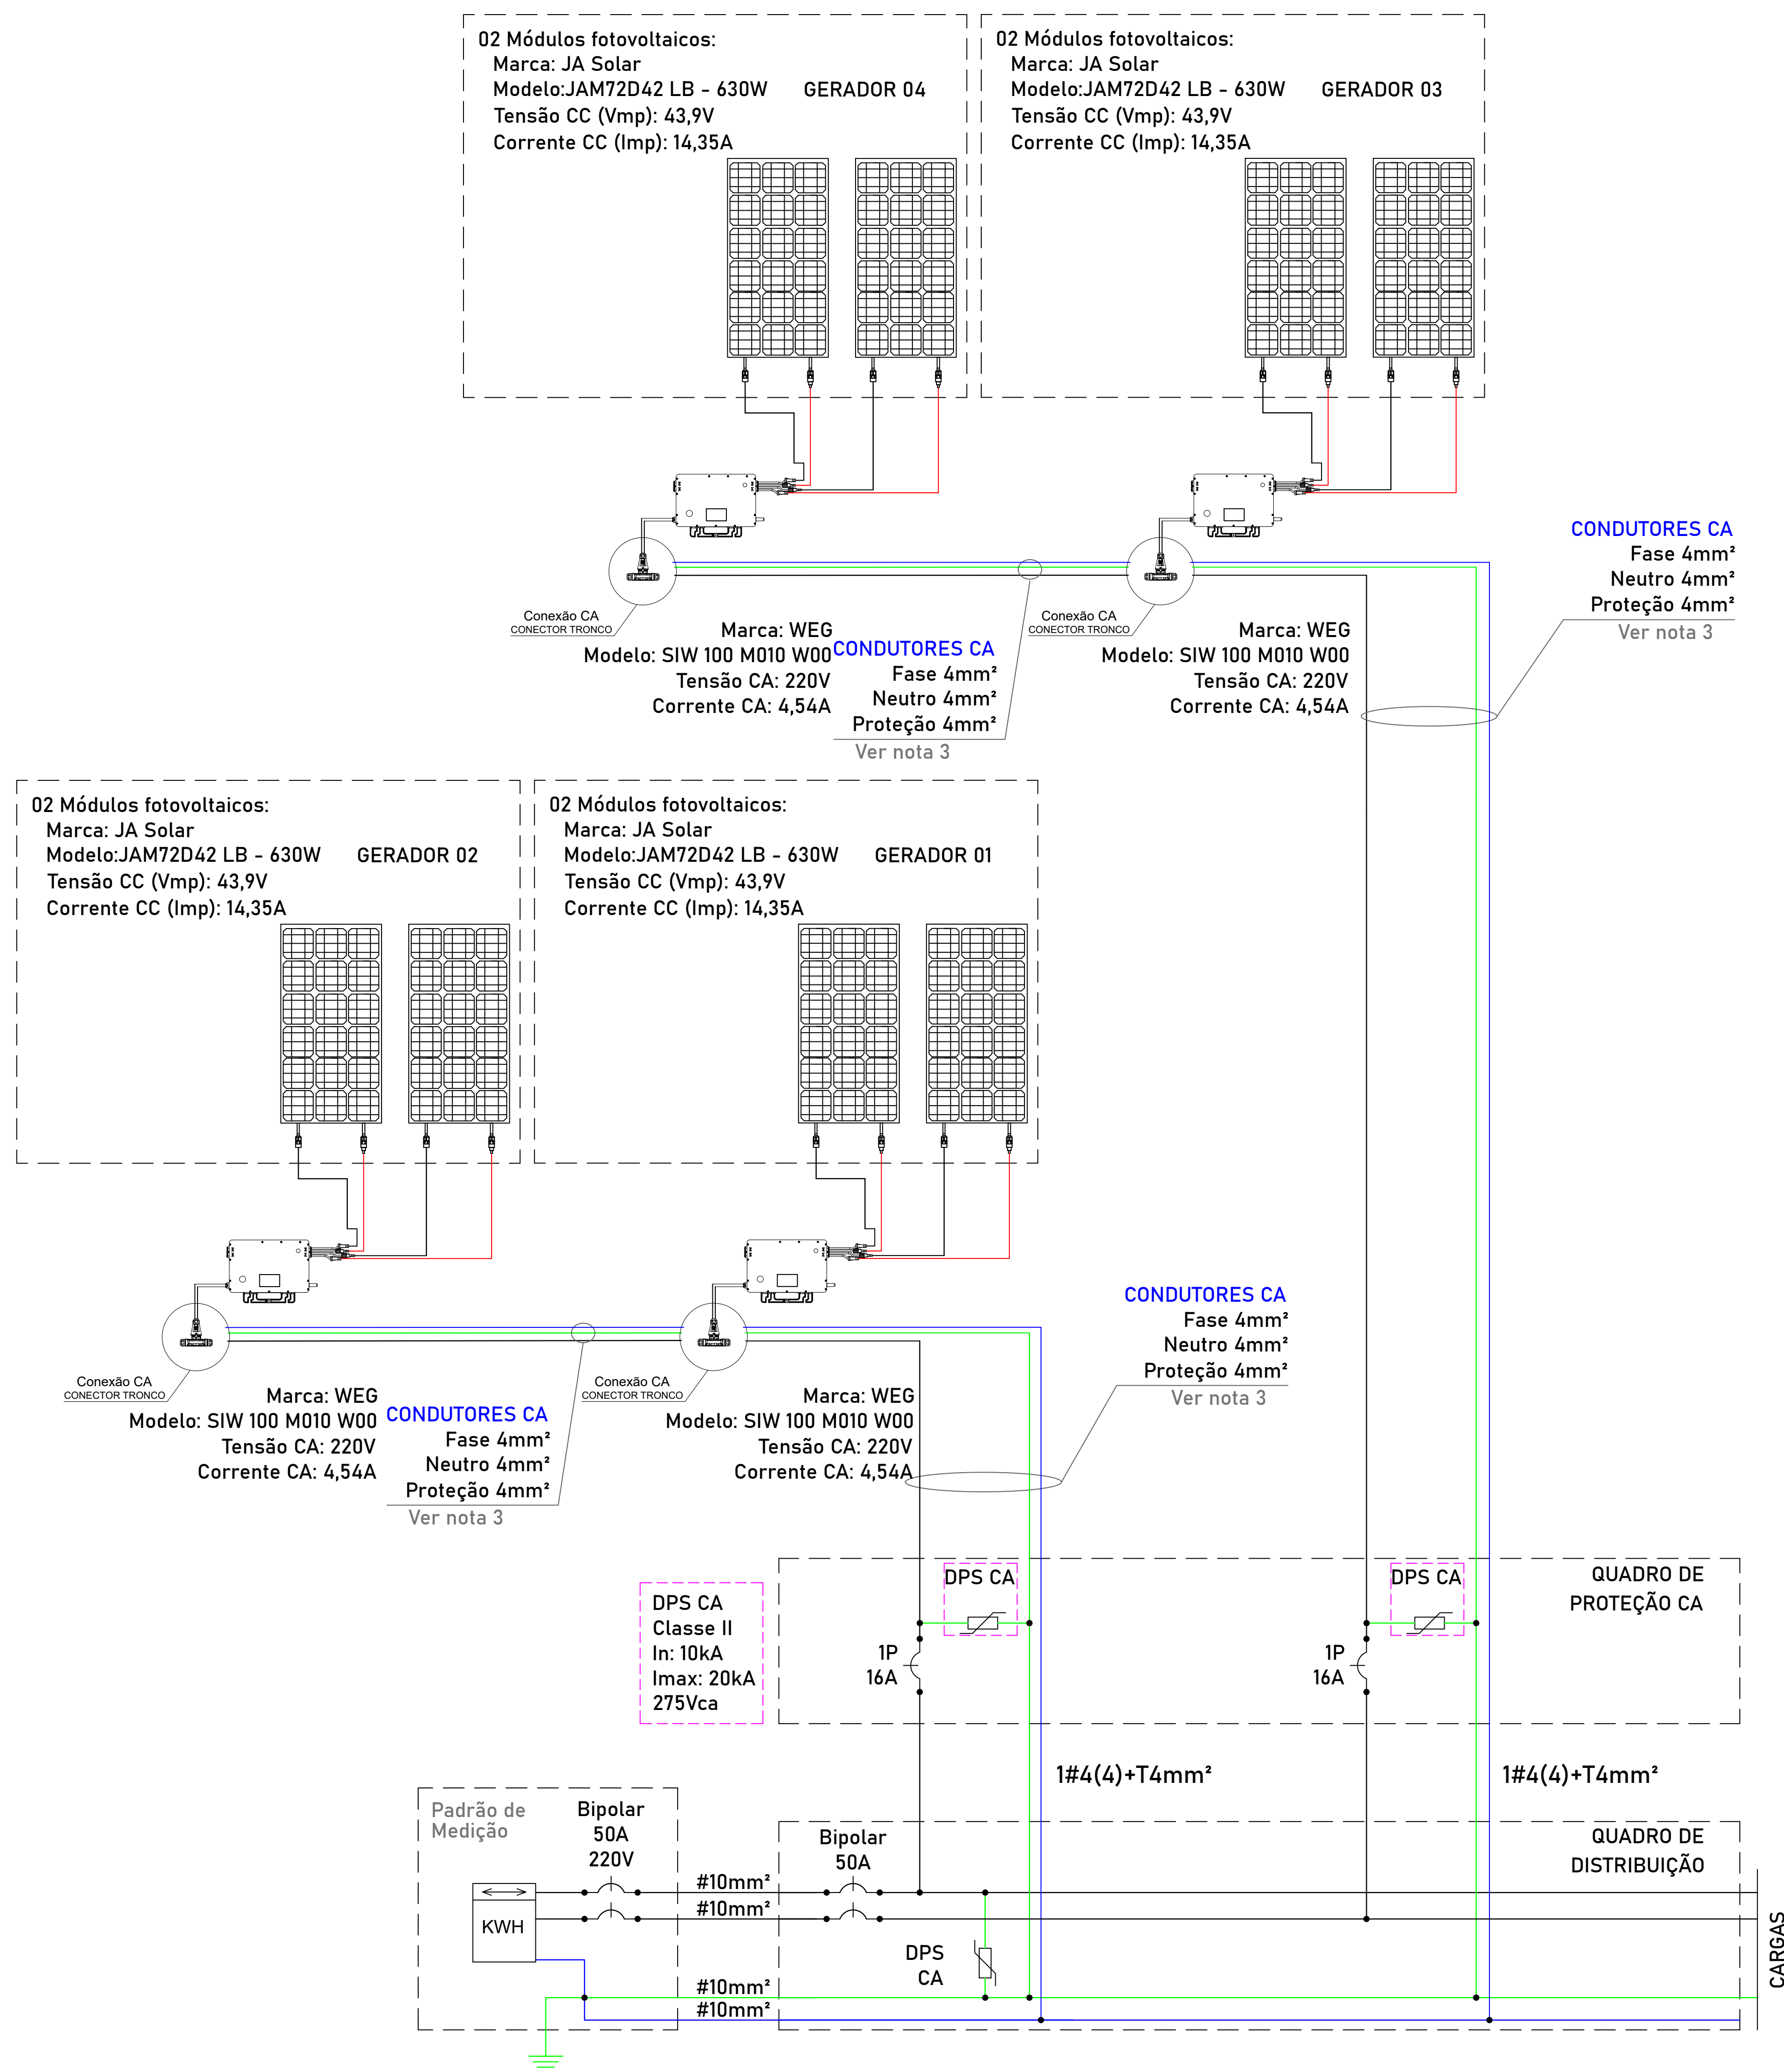

LEGENDA	
	Disjuntor termomagnético
	Medidor de energia kWh
	DPS CC / CA
	Fusível CC
	Barramento
	Transformador / Autotransformador
	Inversor / Microinversor
	Módulo fotovoltaico

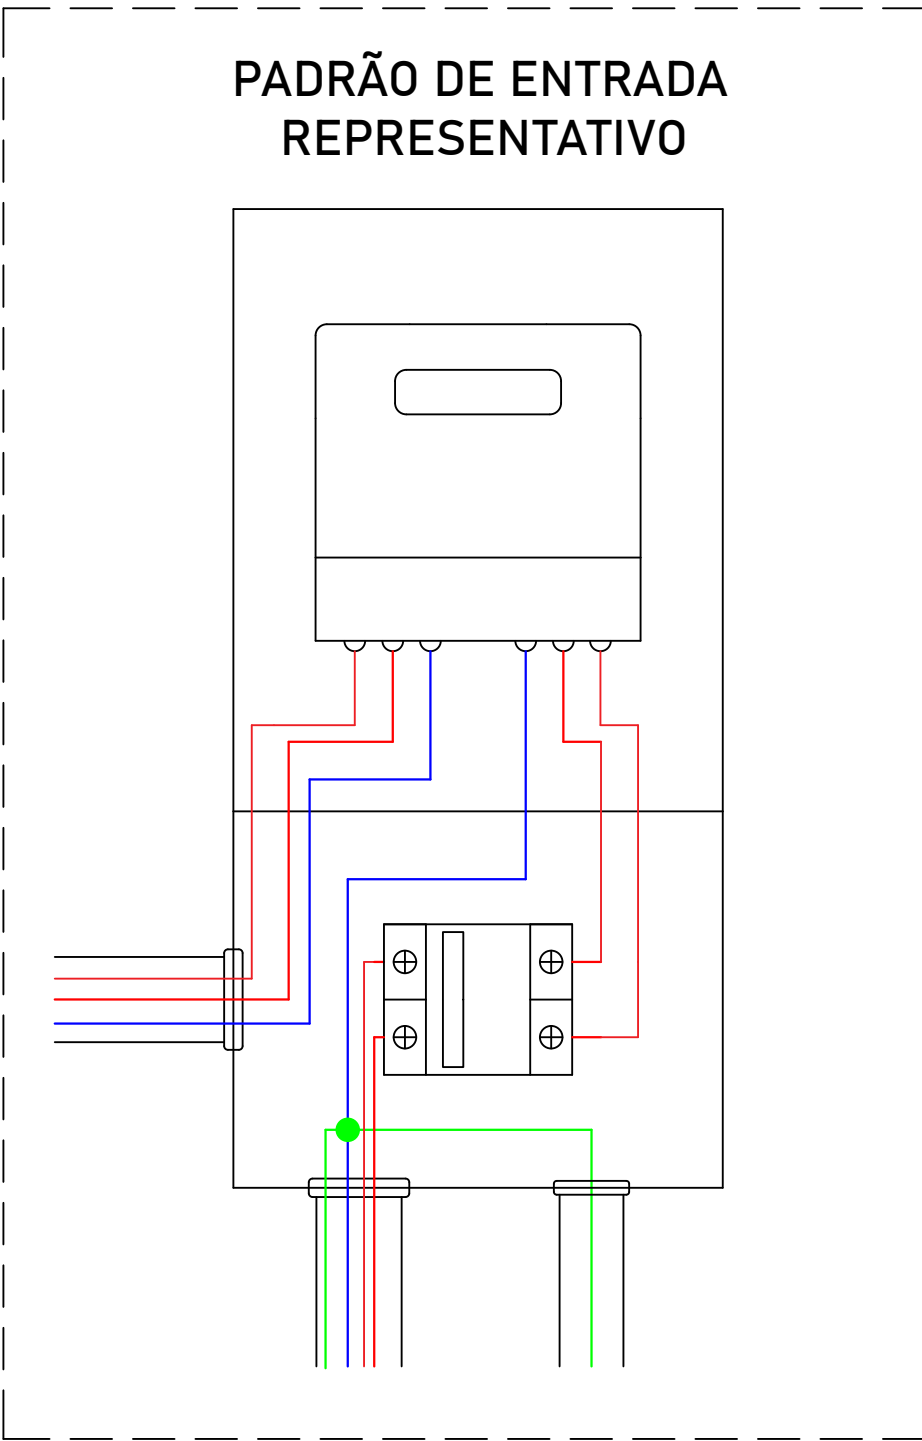


- NOTAS:
1. A seção transversal dos condutores foram dimensionadas em função da corrente máxima de saída e capacidade de condução de corrente, permitindo-se utilizar até uma faixa acima da descrita em cada trecho dessa planta (exceto no padrão de medição);
 2. Cabos em corrente contínua, na tensão elétrica máxima de 1,8kV, isolamento em XLPE e cobertura em XLPE (termofixo) com UV;
 3. Cabos em corrente alternada, na tensão máxima de 1kV, isolamento e cobertura em PCV;
 4. Cada string será protegida individualmente, através das proteções internas do inversor ou por fusível e DPS CC;
 5. A seção transversal dos condutores foram dimensionadas em função da corrente máxima de saída e capacidade de condução de corrente, permitindo-se utilizar até uma faixa acima da descrita em cada trecho dessa planta (exceto no padrão de medição);
 6. Cada MPPT possui apenas uma entrada.



Assinatura do responsável técnico
Guilherme dos Santos de Sena
CFT BA 03321561506


PROJETO:		Sistema fotovoltaico 5,04kWp		PROPRIETÁRIO:	Nome do cliente: Cainan Diego de Andrade CNPJ/CPF: 078.252.929-10	ID do pedido:	3828
TÍTULO:		DIAGRAMA TRIFILAR		ENDEREÇO DA OBRA: Endereço: RUA 06, 403- LOT BR. FELICE, B - AREIAS - TIJUCAS CEP: 88.200-000			
PROJETISTA:	DATA:	REVISADO POR:	REVISÃO:	CONTA CONTRATO:	INTEGRADOR:	FOLHA:	
Diego Lima	17/03/2025	Guilherme Sena	01	55154392	Ekoh	02	

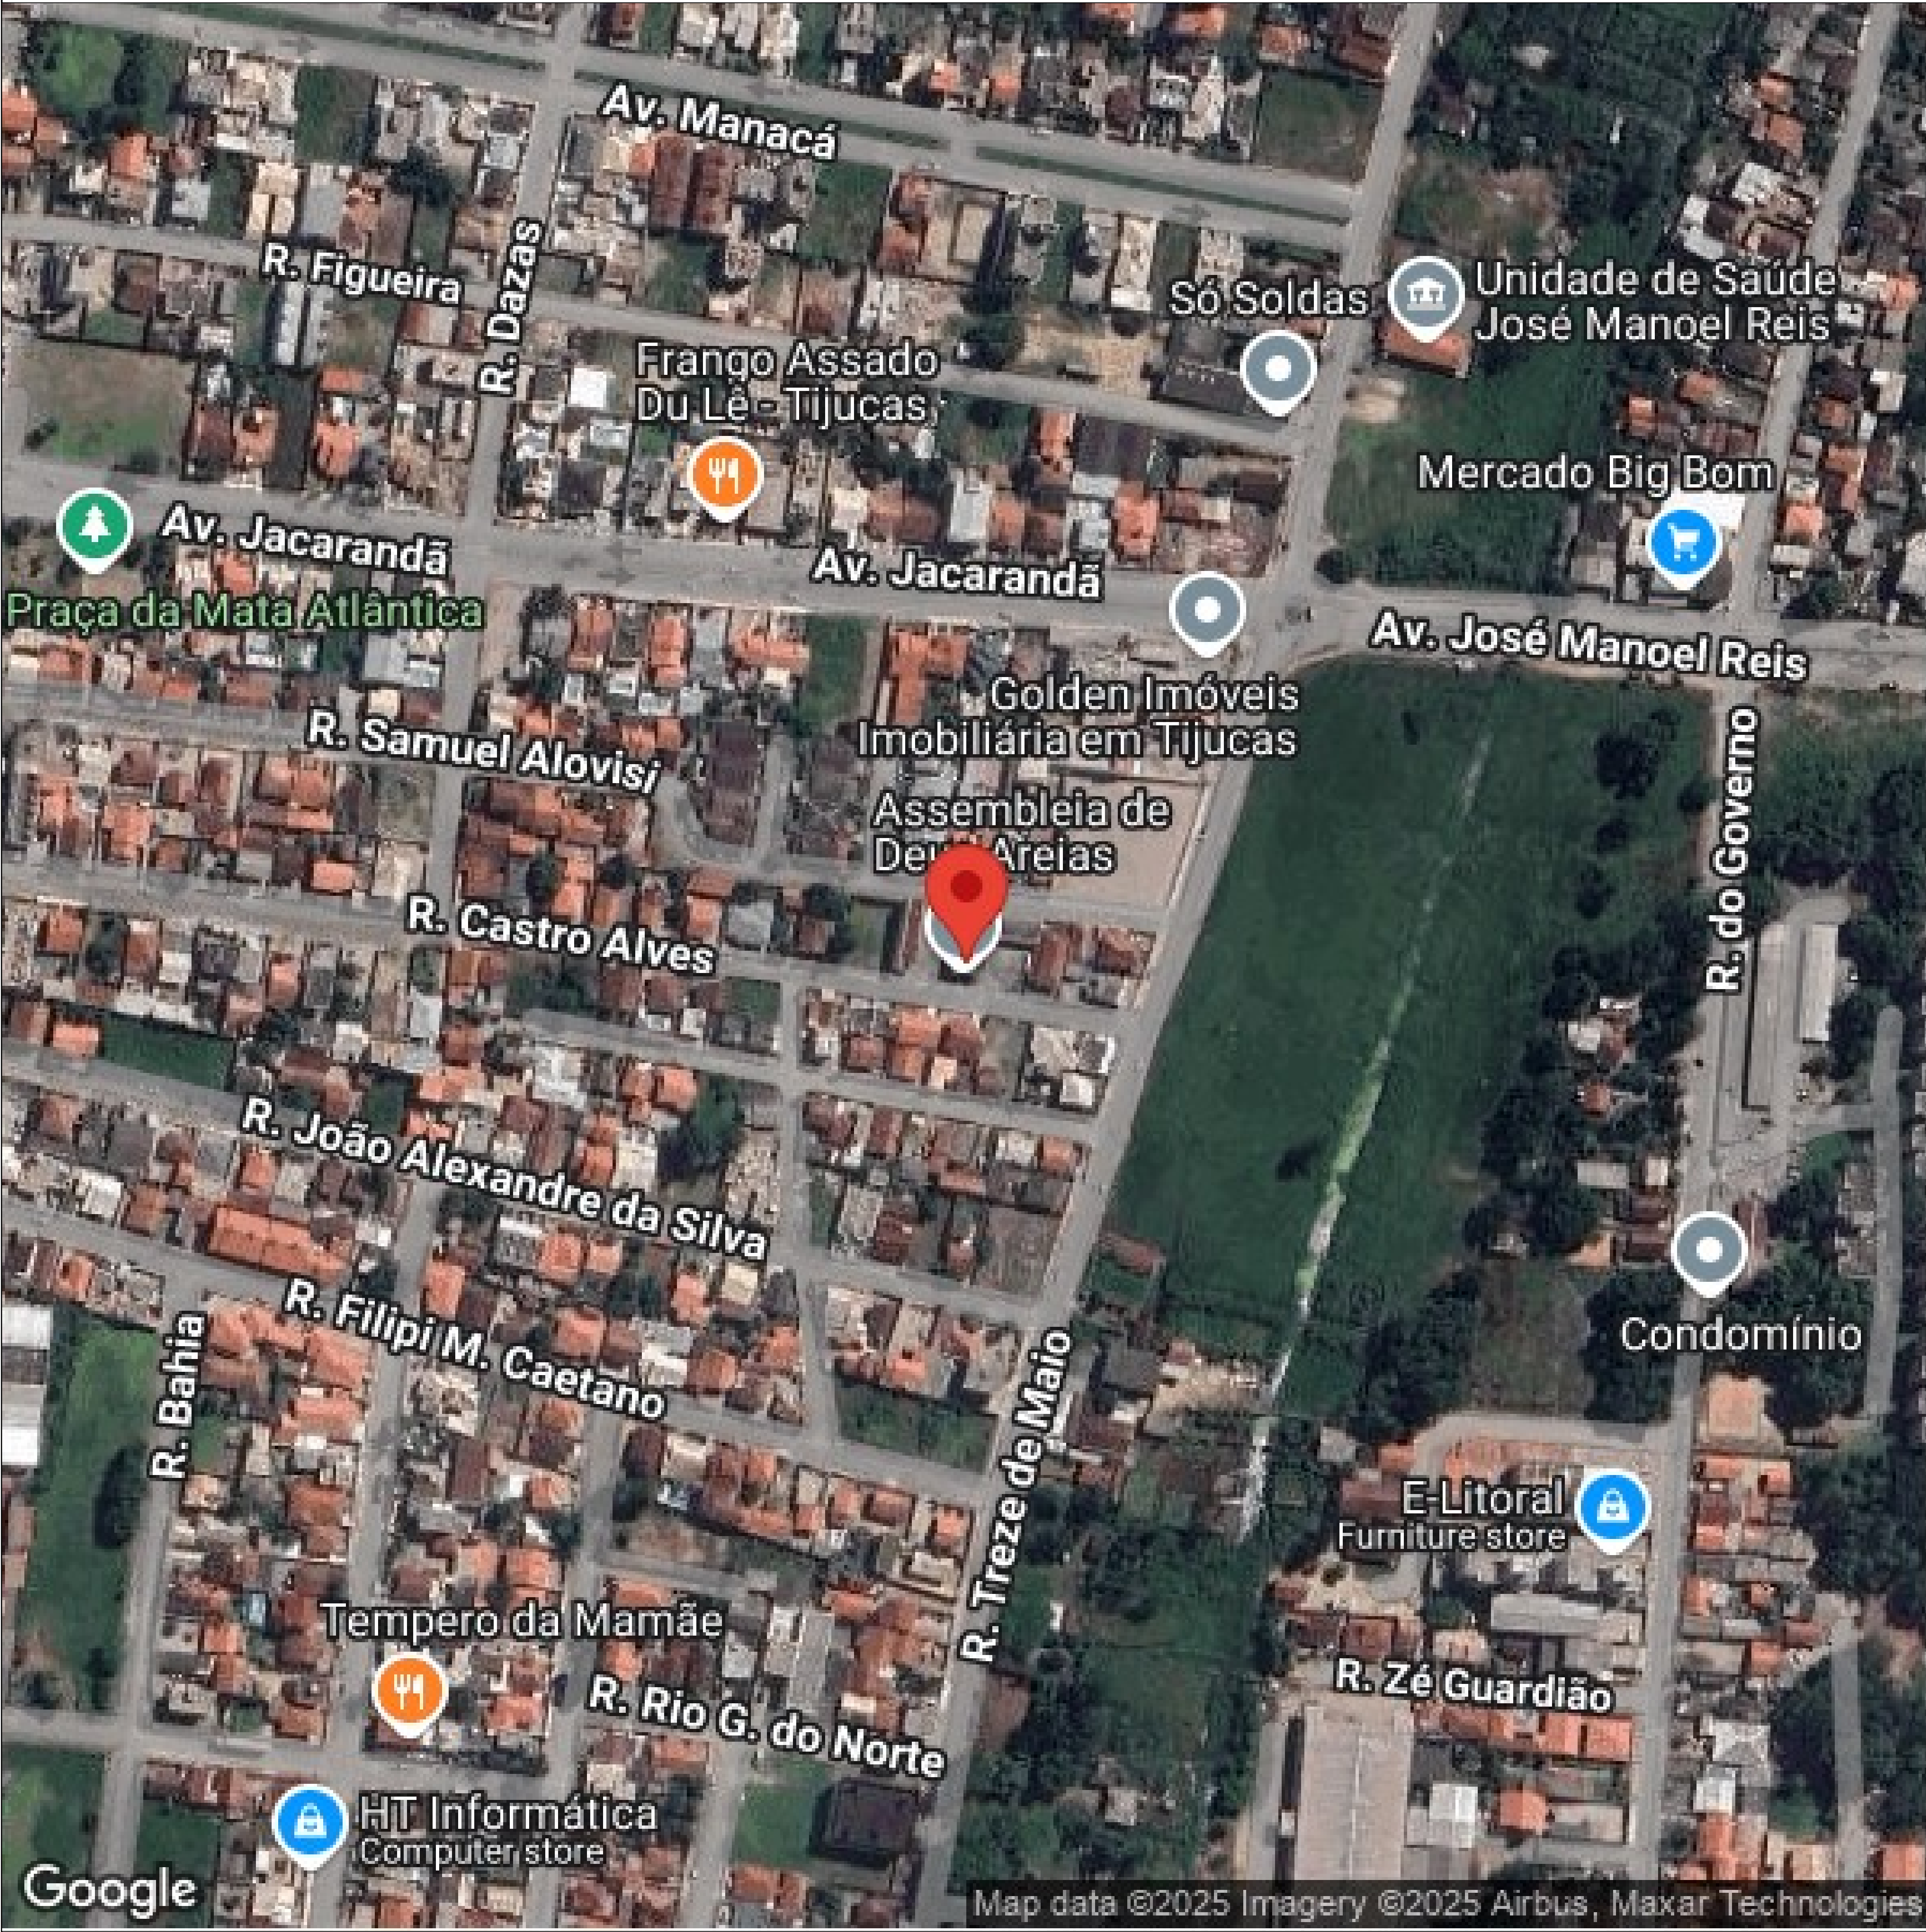



BRASIL

PLATAFORMA DE PROJETOS E ENGENHARIA

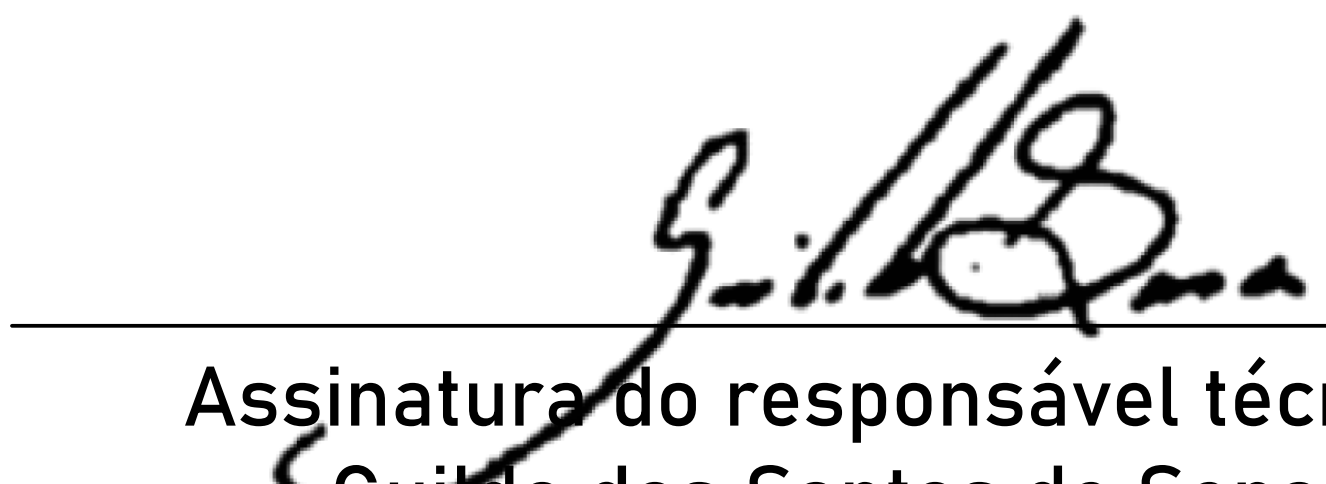

Assinatura do responsável técnico
Guildo dos Santos de Sena
CFT BA 03321561506

PROJETO: Sistema fotovoltaico 5,04kWp				PROPRIETÁRIO: Nome do cliente: Cainan Diego de Andrade CNPJ/CPF: 078.252.929-10		ID do pedido: 3828
TÍTULO: PLANTA DE LOCALIZAÇÃO				ENDEREÇO DA OBRA: Endereço: RUA 06, 403- LOT BR. FELICE, B - AREIAS - TIJUCAS CEP: 88.200-000		
PROJETISTA: Diego Lima	DATA: 17/03/2025	REVISADO POR: Guildo Sena	REVISÃO: 01	CONTA CONTRATO: 55154392	INTEGRADOR: Ekoh	FOLHA: 03



Sua solicitação foi realizada!

O prazo para envio do Orçamento de Conexão é de 15 dias para unidades consumidoras com microgeração em que não haja necessidade de realização de obras no sistema de distribuição ou de transmissão e 30 dias quando houver a necessidade de realização de obras. Para sistemas de minigeração e demais conexões o prazo é de 45 dias.

Seu número de protocolo é

8033913145



[Voltar para a página inicial](#)

Sua opinião é valiosa!

[Preencha nossa pesquisa de satisfação e ajude-nos a aprimorar sua experiência.](#)

